


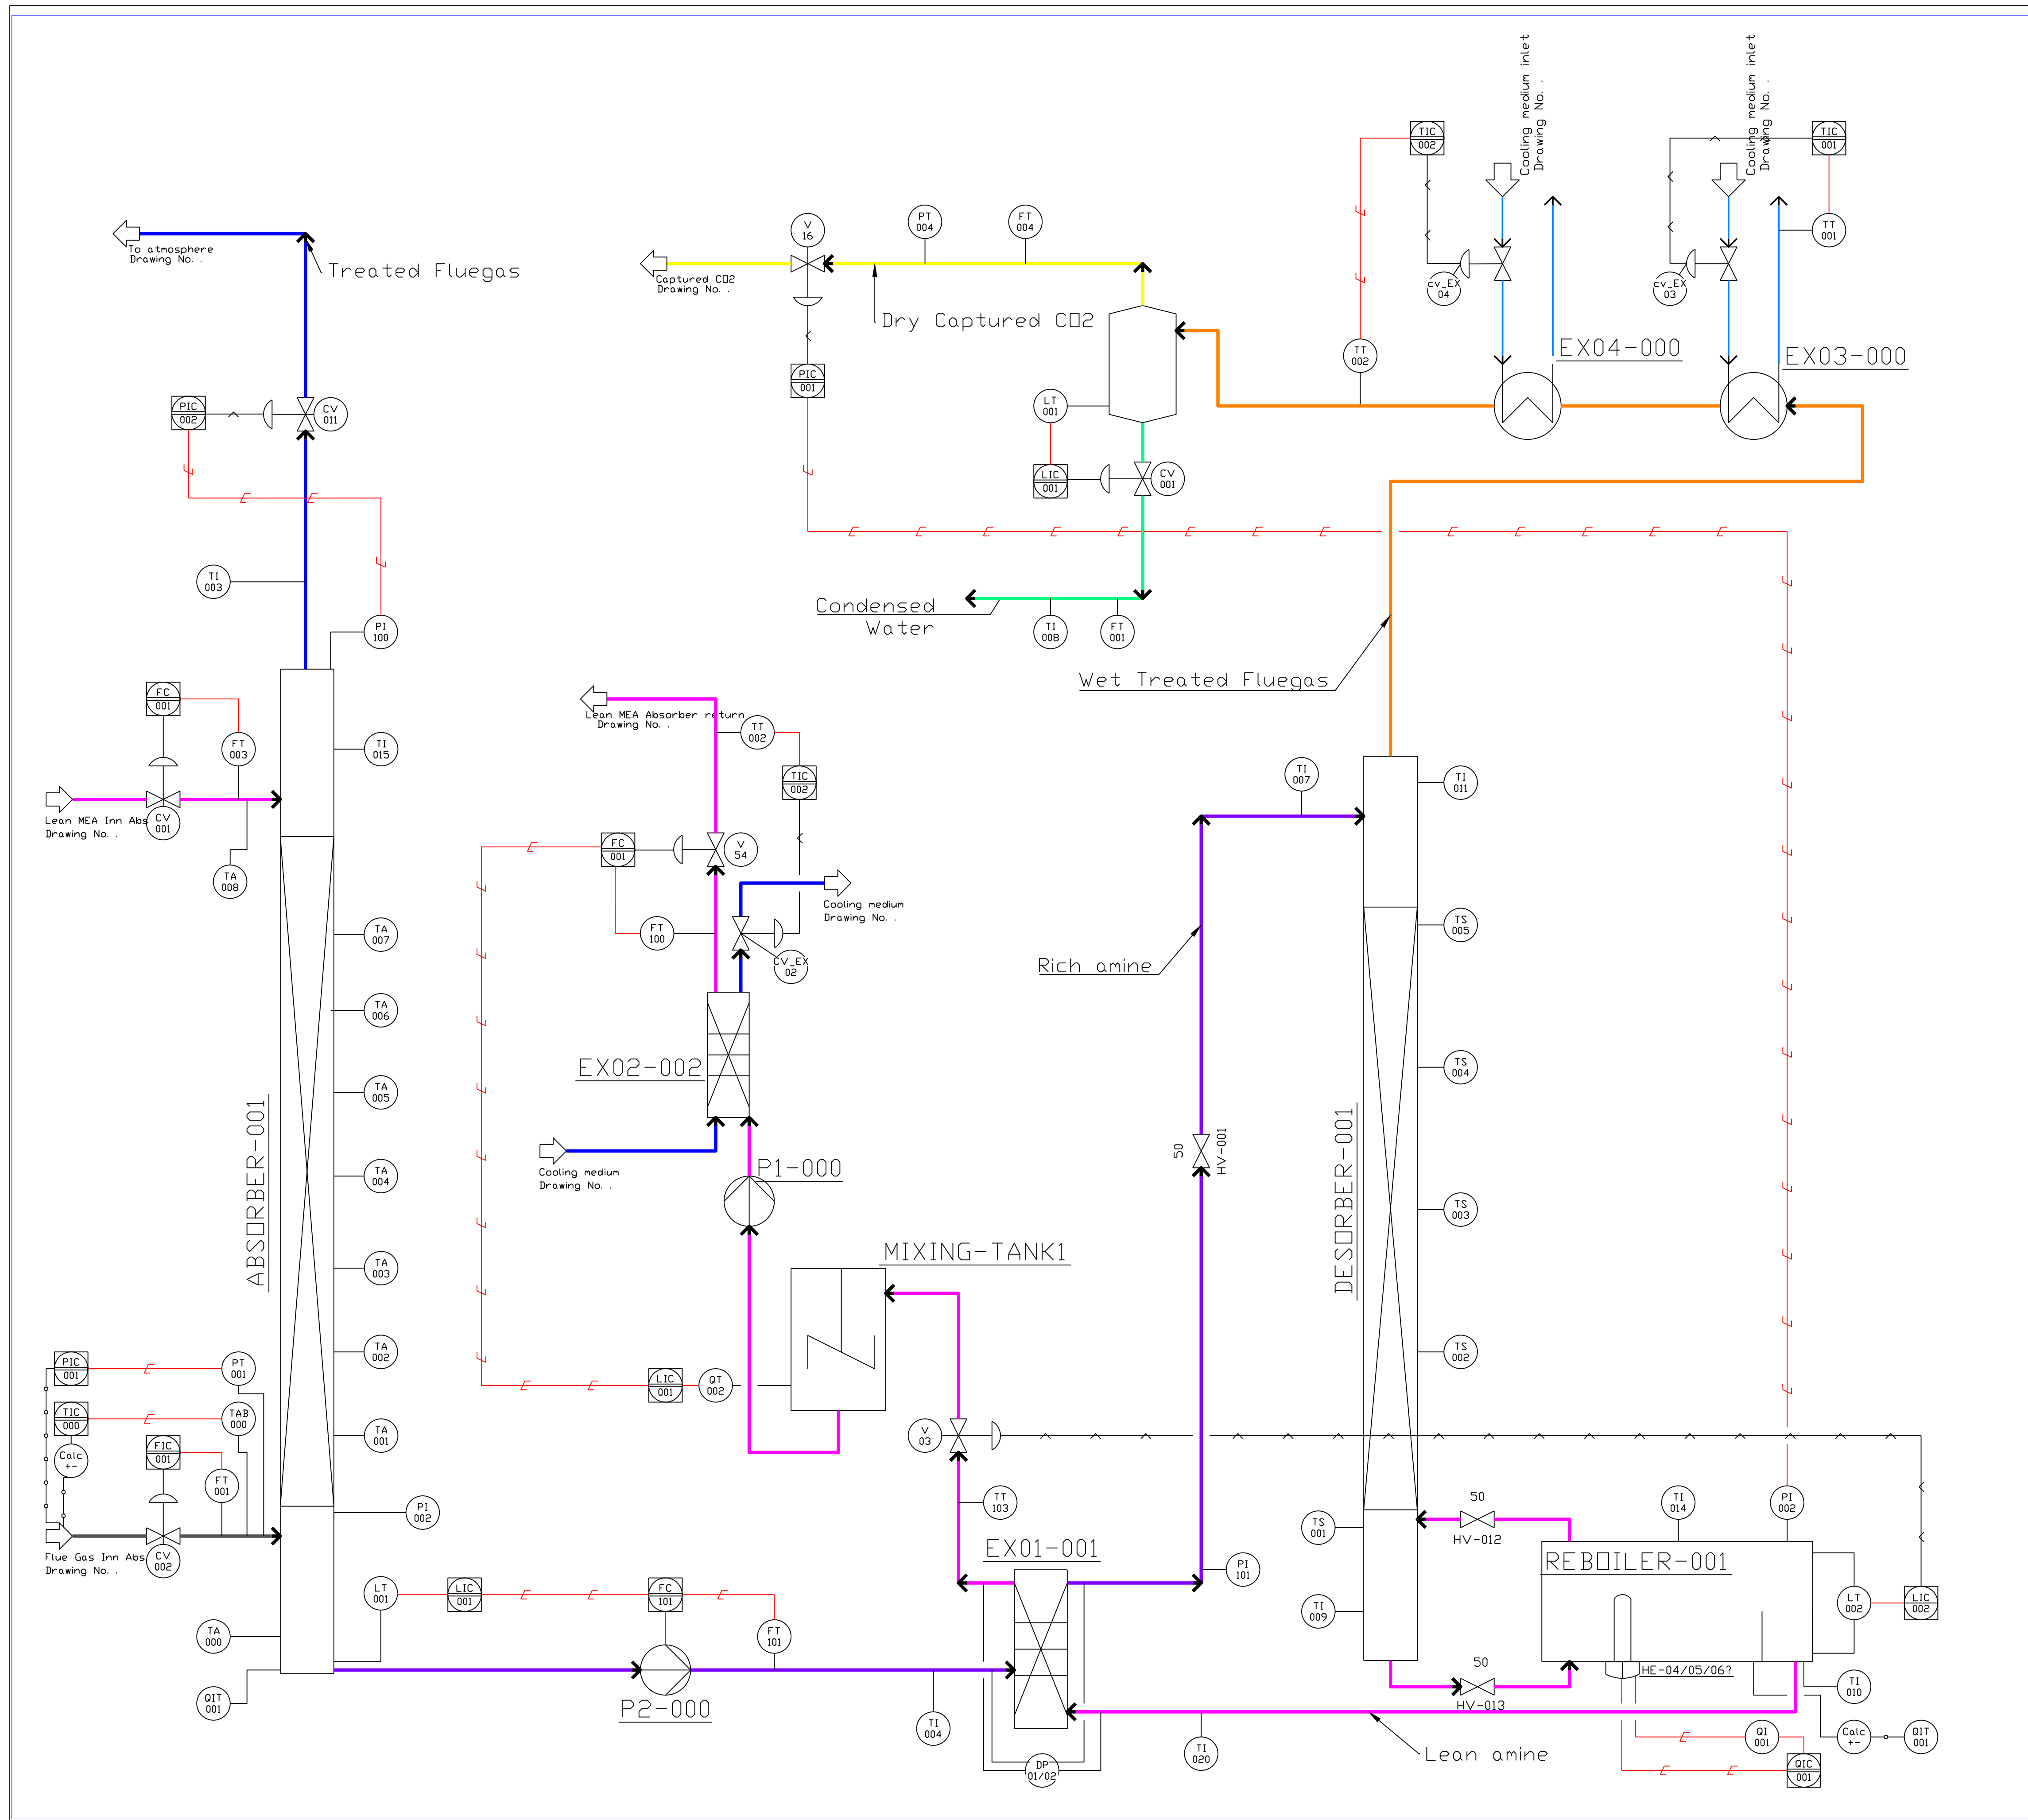

General Notes

Area codes for equipment:
00 = Absorber
01 = Desorber
02 = Reboiler and mixing tank
03 = Cooler EX03
04 = Cooler EX04 and Condenser.

No.	Revision/Issue	Date

Drawing Name

Project Name and Address

Gløshaugen K-Spice
Teknisk prosess
flytskjema

Area	Stamp
Drawing Number	
Author	
Ruben	